


| LEGEND      |                 |
|-------------|-----------------|
| <div></div> | EXISTING LEVEL  |
| <div></div> | FORMATION LEVEL |
| <div></div> | DESIGN LEVEL    |

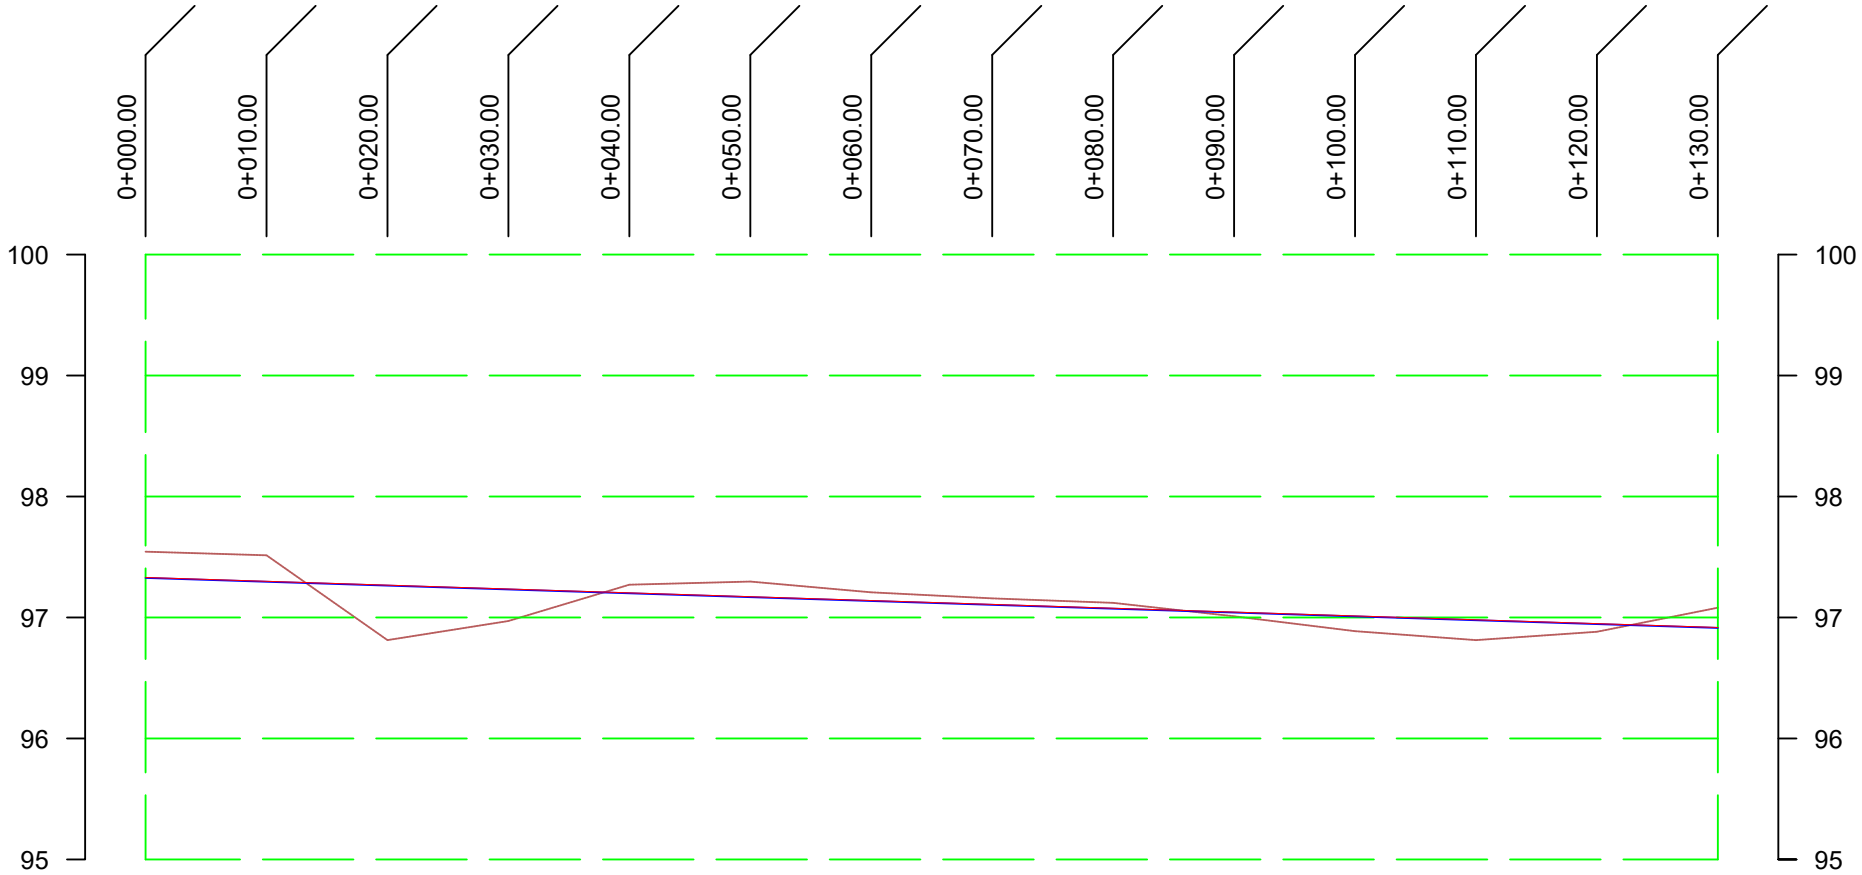

|                        |          |          |          |          |          |          |          |          |          |          |          |          |          |          |
|------------------------|----------|----------|----------|----------|----------|----------|----------|----------|----------|----------|----------|----------|----------|----------|
| FORMATION<br>LEVEL (m) | 97.333   | 97.298   | 97.265   | 97.231   | 97.197   | 97.163   | 97.129   | 97.095   | 97.061   | 97.027   | 96.993   | 96.959   | 96.925   | 96.891   |
| EXISTING<br>LEVEL (m)  | 97.544   | 97.514   | 96.813   | 96.971   | 97.271   | 97.297   | 97.208   | 97.158   | 97.121   | 97.010   | 96.887   | 96.813   | 96.882   | 97.081   |
| CHAINAGE (km)          | 0+000.00 | 0+010.00 | 0+020.00 | 0+030.00 | 0+040.00 | 0+050.00 | 0+060.00 | 0+070.00 | 0+080.00 | 0+090.00 | 0+100.00 | 0+110.00 | 0+120.00 | 0+130.00 |

CHAINAGE : 0+000.00 - 0+130.00

|   |  |                 |   |          |                |                              |                          |   |  |
|---|--|-----------------|---|----------|----------------|------------------------------|--------------------------|---|--|
| NAME / GROUP NAME : Mr. Sukith Siriwardana/ GROUP 01   |  | DRAWING DETAILS |   |          |                | DRAWING TITLE                |                          | DEPARTMENT OF CIVIL<br>ENGINEERING<br>FACULTY OF ENGINEERING<br>GENERAL SIR JOHN KOTELAWALA<br>DEFENCE UNIVERSITY |  |
| GROUP MEMBERS :<br>D/ENG/23/0078/CE NMYP Premaratne<br>D/ENG/24/0020/CE B.Banujan<br>D/ENG/24/0112/CE M.F.Hasni Ahamed<br>D/ENG/24/0038/CE GDTD Jayawardena<br>D/ENG/24/0077/CE MKCK Madawala<br>D/ENG/24/0104/CE KKVYA Vidanage |  | DATE            | 2025/10/30   | SCALE    | 16:1           | LONGITUDINAL SECTION OF ROAD |                          |   |  |
|   |  | LOCATION        | COMBAT TRAINING AREA,SLNS VIDURA,<br>EASTERN NAVAL COMMAND BASE,<br>SAMPOOR TRINCOMALEE.   | CHAINAGE | 0+000 TO 0.130 | PROJECT                      |                          |   |  |
|   |  | NOTES           | This drawing and related data are part of an academic survey and design study conducted for educational purposes at SLNS Vidura. The information contained herein is not to be copied, distributed, or used for any purpose other than project evaluation without prior written permission from the supervising authorities and the Department of Civil Engineering,KDU. |          |                |                              | SURVEY CAMP<br>INTAKE 41 |   |  |
|   |  |                 |   |          |                |                              |                          |   |  |