


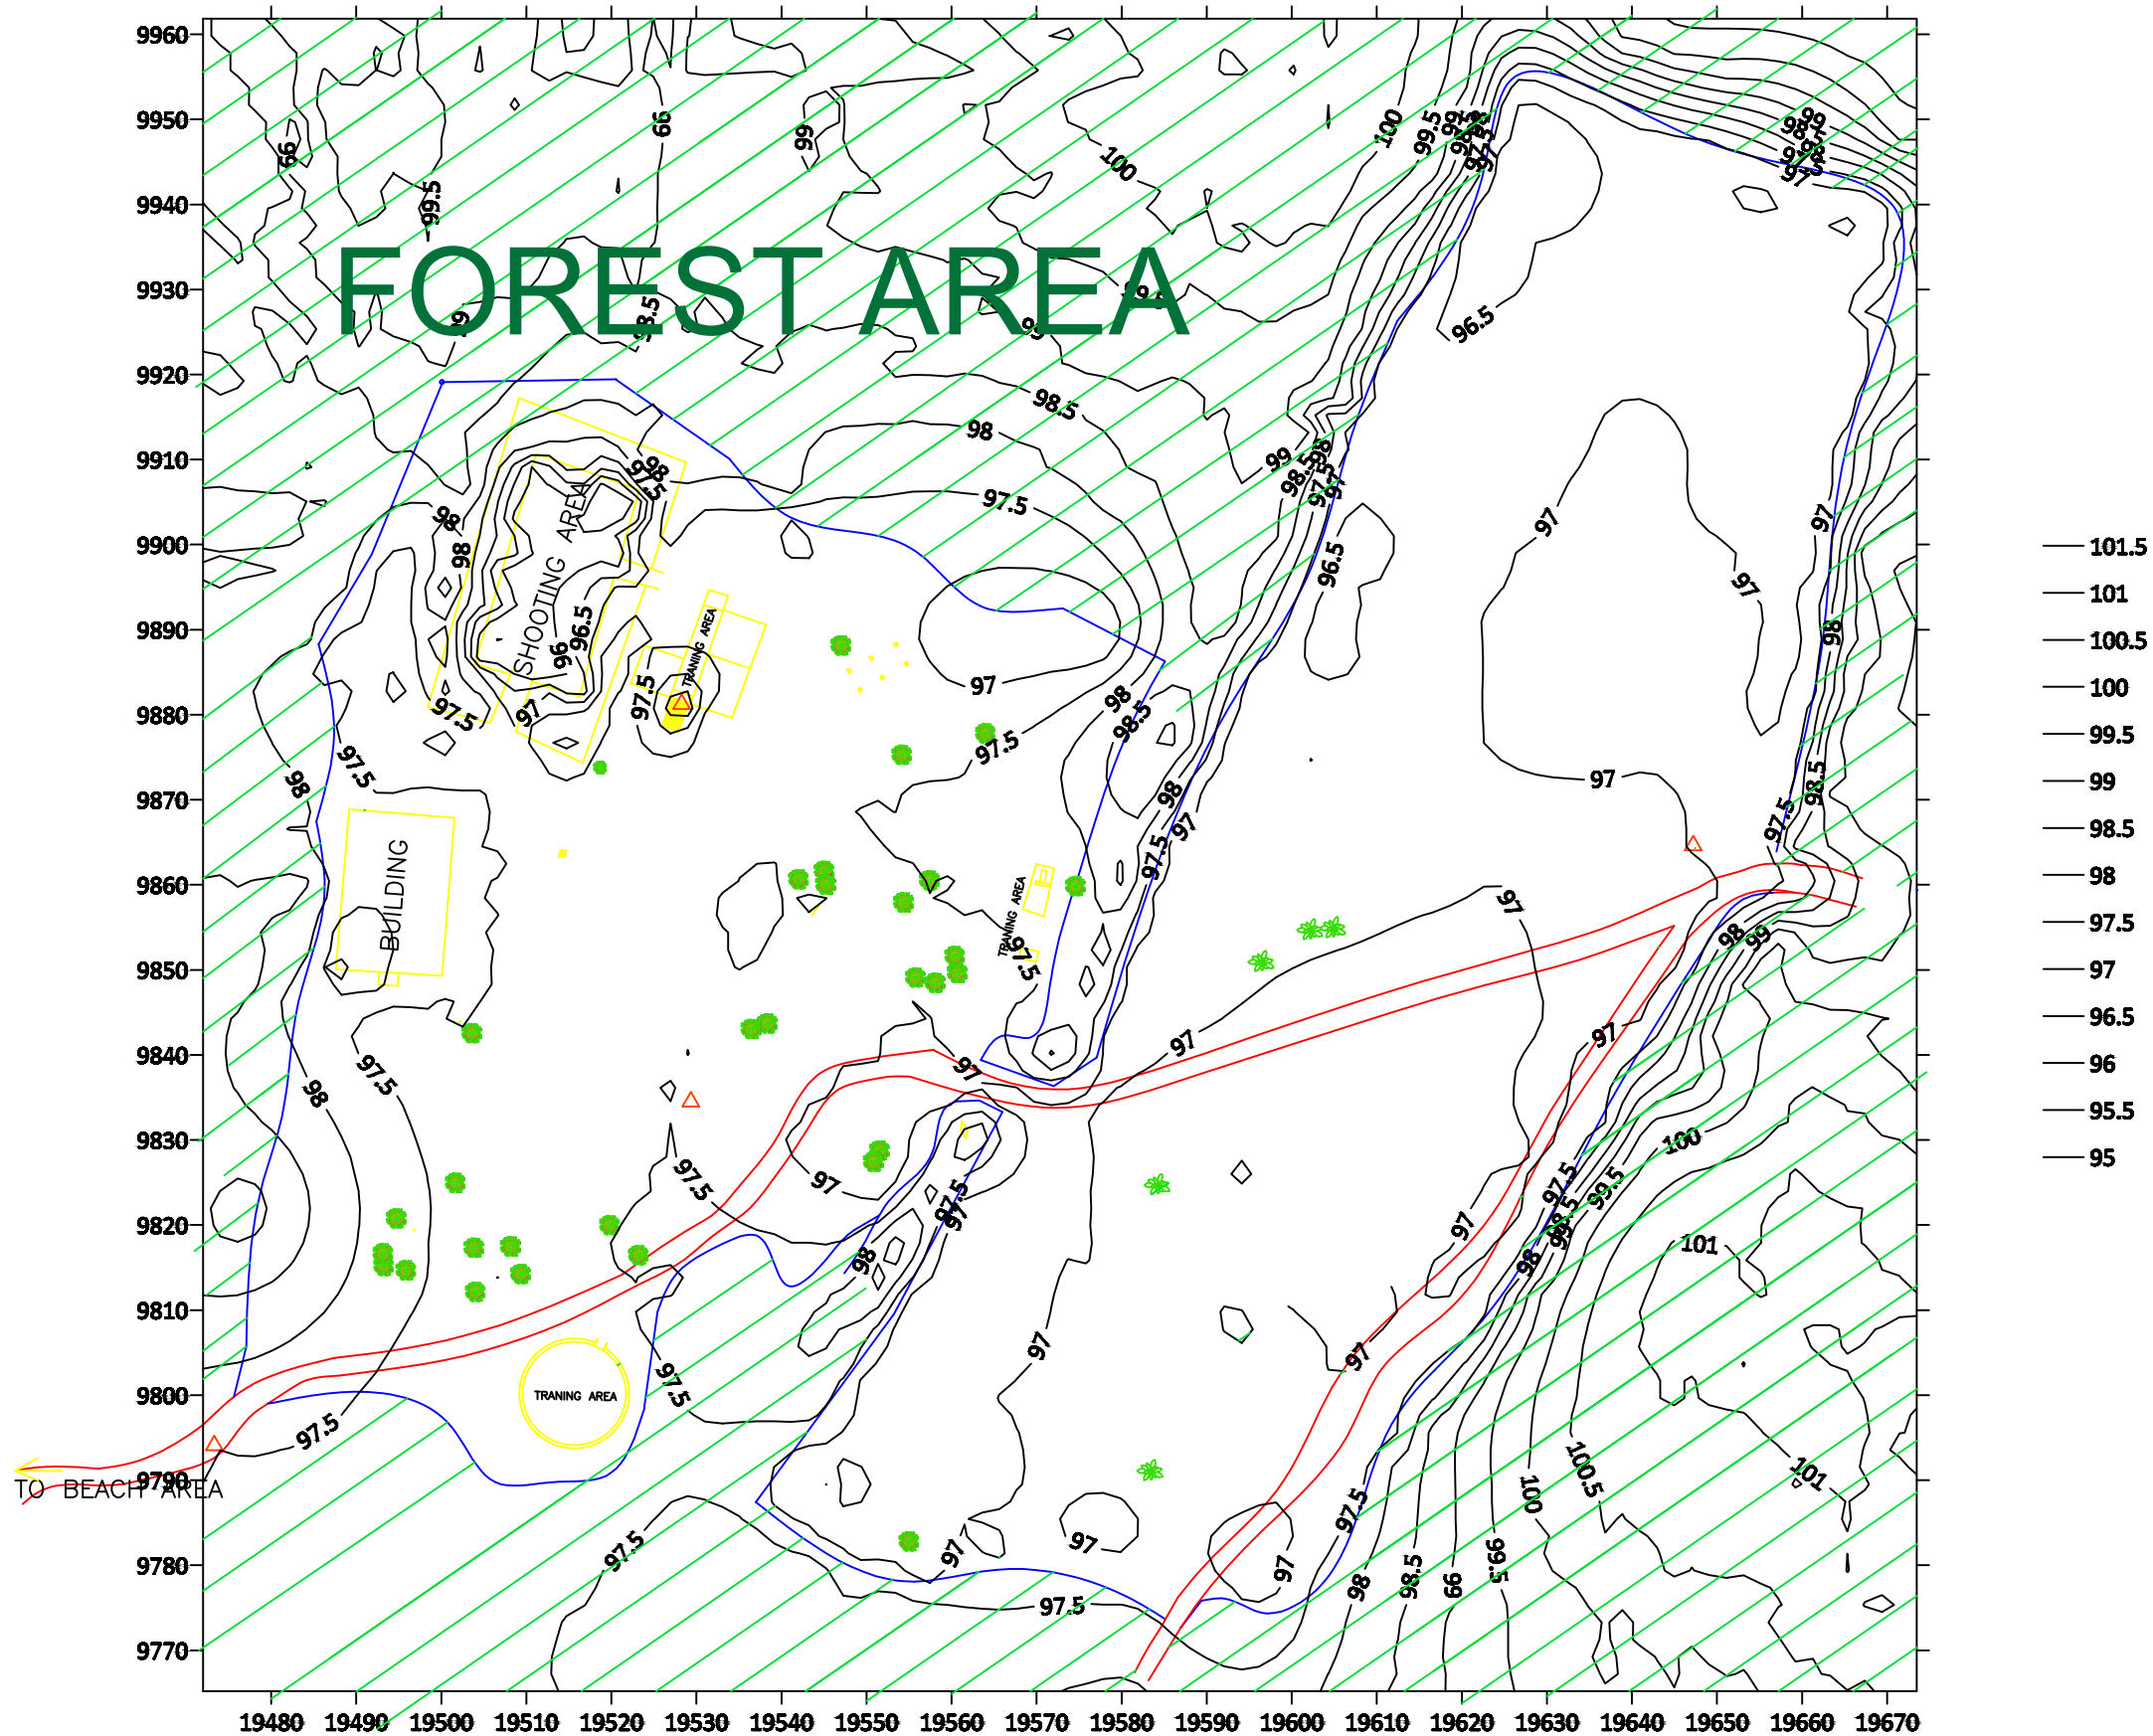

NAME / GROUP NAME : Mr. Sukith Siriwardana/ GROUP 01

GROUP MEMBERS : D/ENG/23/0078/CE NMYP Premaratne
D/ENG/24/0020/CE B.Banujan
D/ENG/24/0112/CE M.F.Hasni Ahamed
D/ENG/24/0038/CE GDTD Jayawardena
D/ENG/24/0077/CE MKCK Madawala
D/ENG/24/0104/CE KKVYA Vidanage

DRAWING DETAILS

DATE	2025/10/30	UNITS	METERS
LOCATION	COMBAT TRAINING AREA,SLNS VIDURA, EASTERN NAVAL COMMAND BASE, SAMPOOR TRINCOMALEE.	DRAWING NO.	04
NOTES	This drawing and related data are part of an academic survey and design study conducted for educational purposes at SLNS Vidura. The information contained herein is not to be copied, distributed, or used for any purpose other than project evaluation without prior written permission from the supervising authorities and the Department of Civil Engineering,ADU.		

DRAWING TITLE

TOPOGRAPHICAL DETAIL PLAN
PROJECT
SURVEY CAMP INTAKE 41

DEPARTMENT OF CIVIL
ENGINEERING
FACULTY OF ENGINEERING
GENERAL SIR JOHN KOTELAWALA
DEFENCE UNIVERSITY