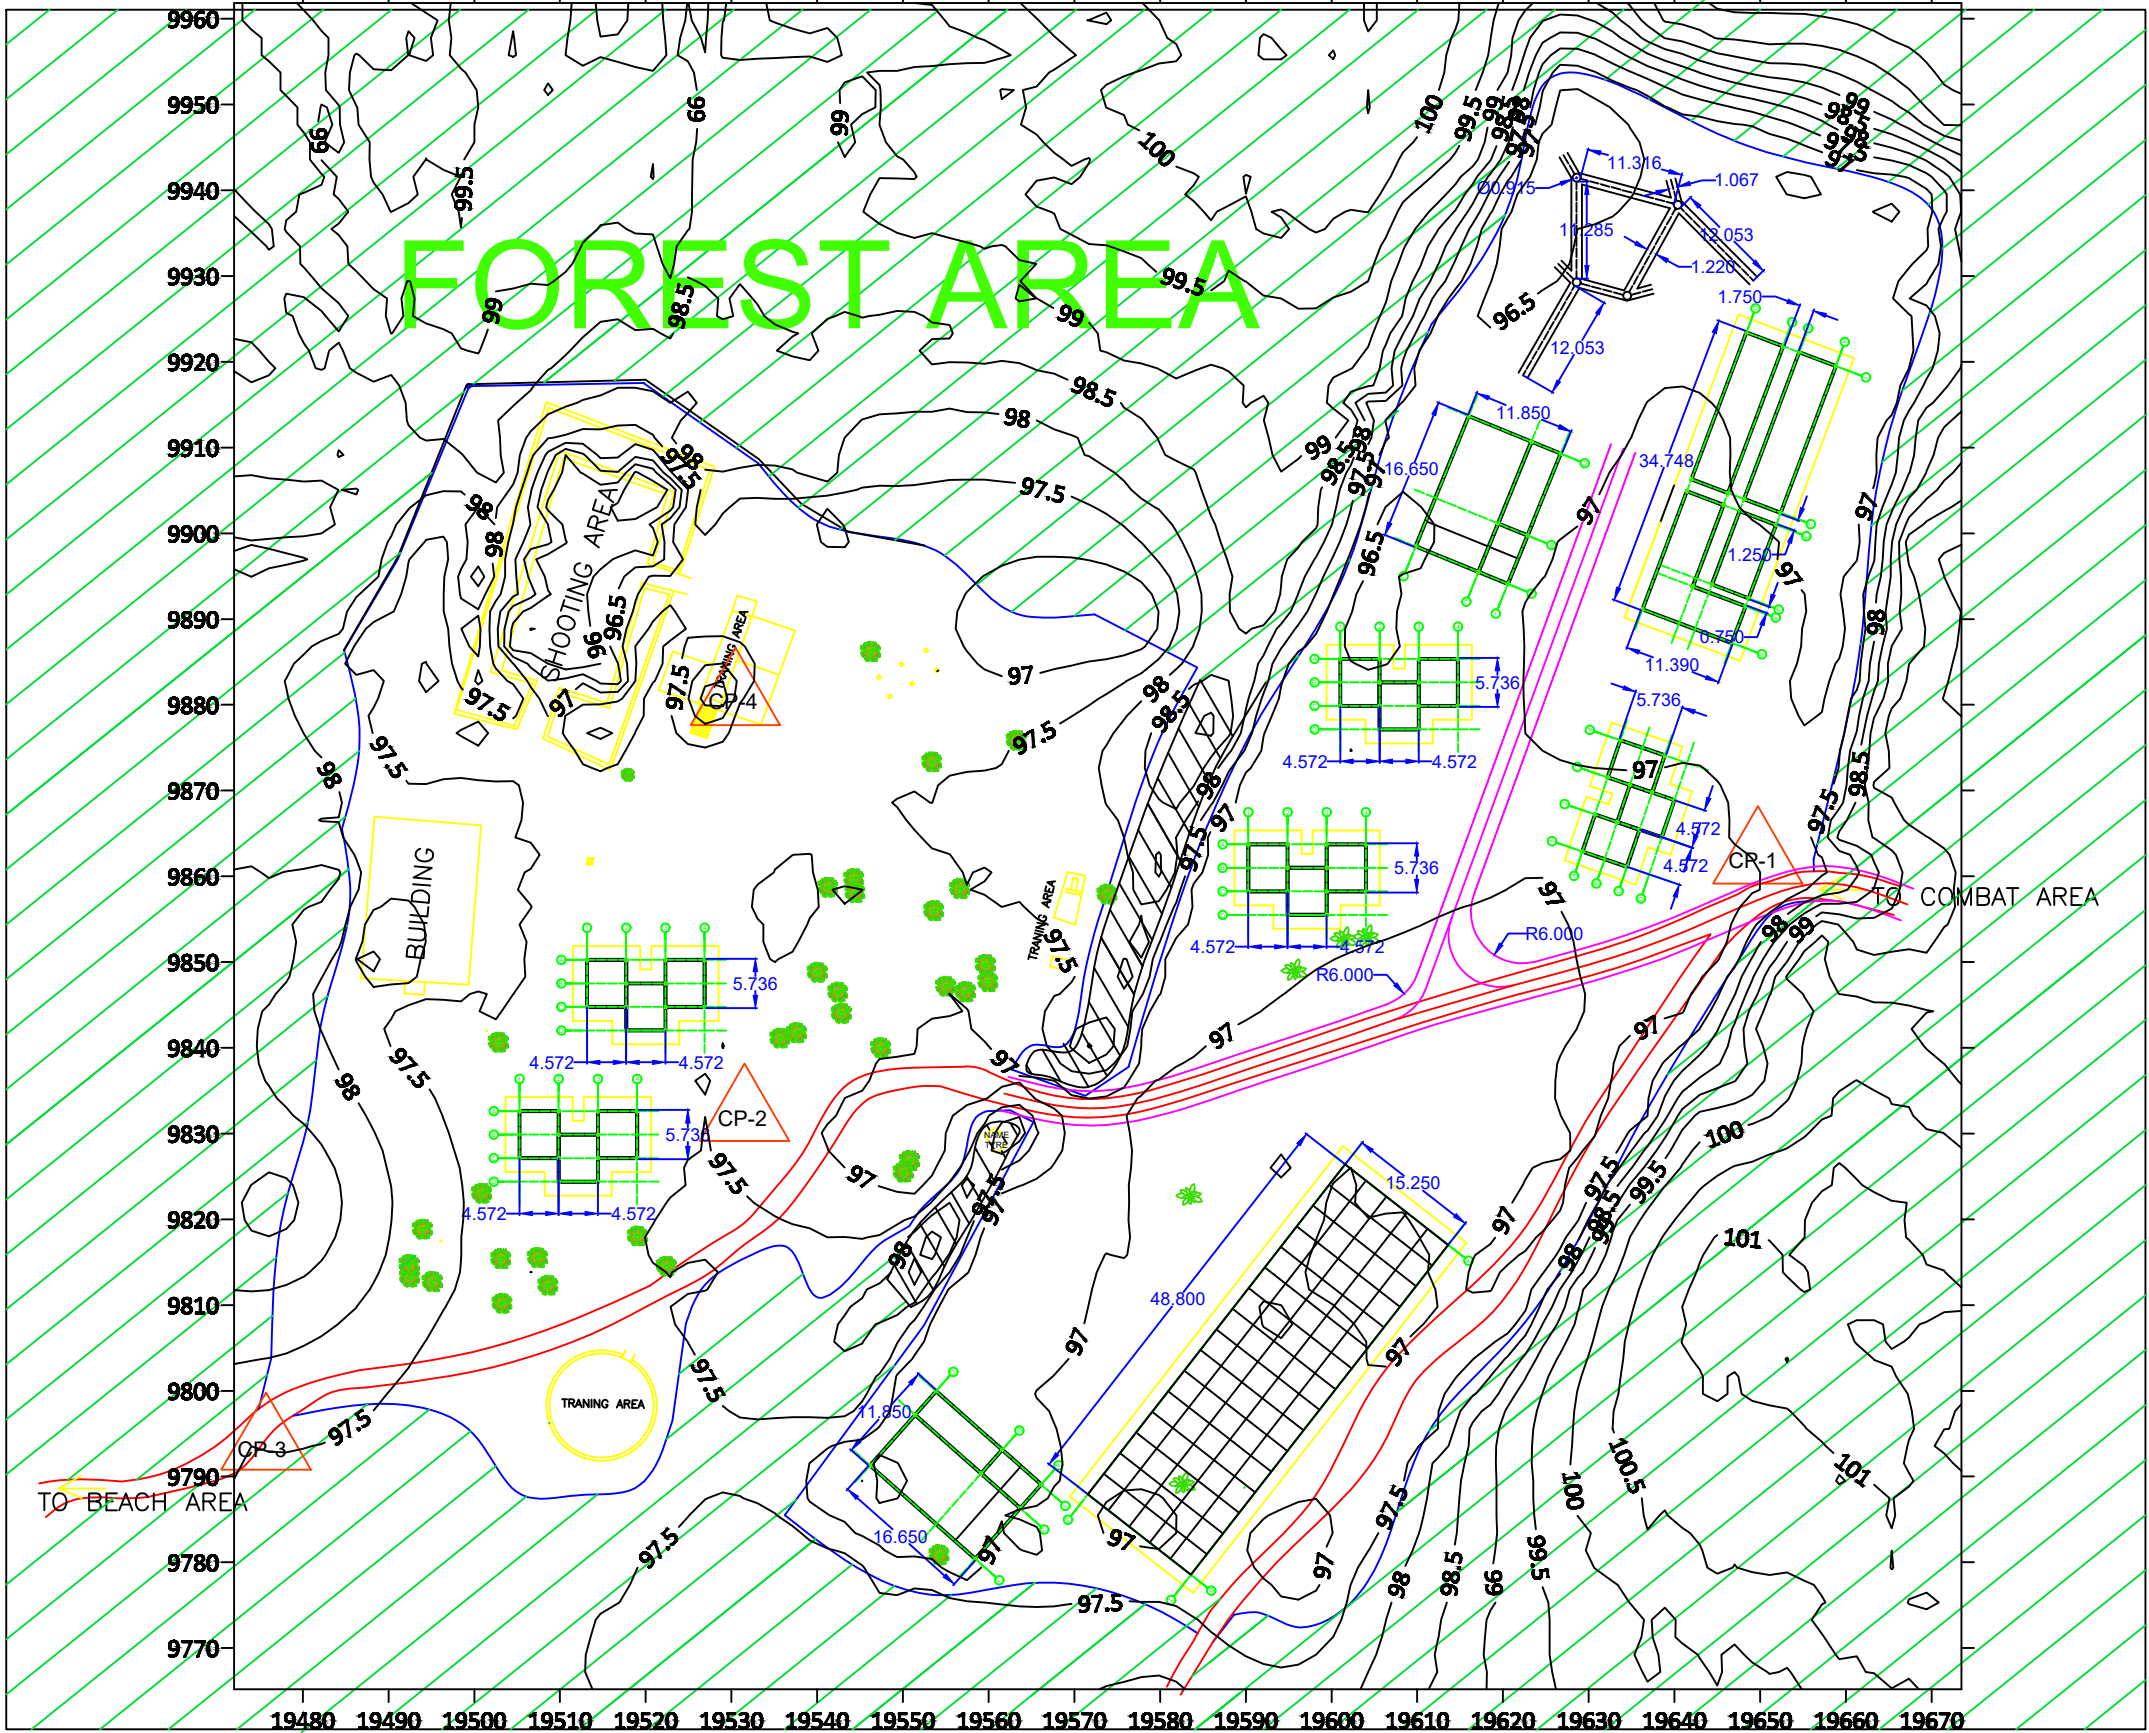


## LEGEND

| BLOCK | Block Name                |
|-------|---------------------------|
|       | BUSH                      |
|       | SMALL TREE                |
|       | ROAD                      |
|       | TREE                      |
|       | CONTROL POINT             |
|       | SAND DUNE                 |
|       | FOREST                    |
|       | TOWER                     |
|       | CENTER LINE               |
|       | PROPOSED ROAD             |
|       | PROPOSED ROAD CENTER LINE |

NAME / GROUP NAME : Mr. Sukith Siriwardana/ GROUP 01

GROUP MEMBERS :  
D/ENG/23/0078/CE NMYP Premaratne  
D/ENG/24/0020/CE B.Banujan  
D/ENG/24/0112/CE M.F.Hasni Ahamed  
D/ENG/24/0038/CE GDTD Jayawardena  
D/ENG/24/0077/CE MKCK Madawala  
D/ENG/24/0104/CE KKVYA Vidanage

### DRAWING DETAILS

|          |   |             |        |
|----------|---|-------------|--------|
| DATE     | 2025/10/30   | UNITS       | METERS |
| LOCATION | COMBAT TRAINING AREA,SLNS VIDURA,<br>EASTERN NAVAL COMMAND BASE,<br>SAMPOOR TRINCOMALEE.   | DRAWING NO. | 06     |
| NOTES    | This drawing and related data are part of an academic survey and design study conducted for educational purposes at SLNS Vidura. The information contained herein is not to be copied, distributed, or used for any purpose other than project evaluation without prior written permission from the supervising authorities and the Department of Civil Engineering,ADU. |             |        |

### DRAWING TITLE

|                           |
|---------------------------|
| PROPOSED COMBAT AREA PLAN |
| PROJECT                   |
| SURVEY CAMP<br>INTAKE 41  |

DEPARTMENT OF CIVIL  
ENGINEERING  
FACULTY OF ENGINEERING  
GENERAL SIR JOHN KOTELAWALA  
DEFENCE UNIVERSITY