


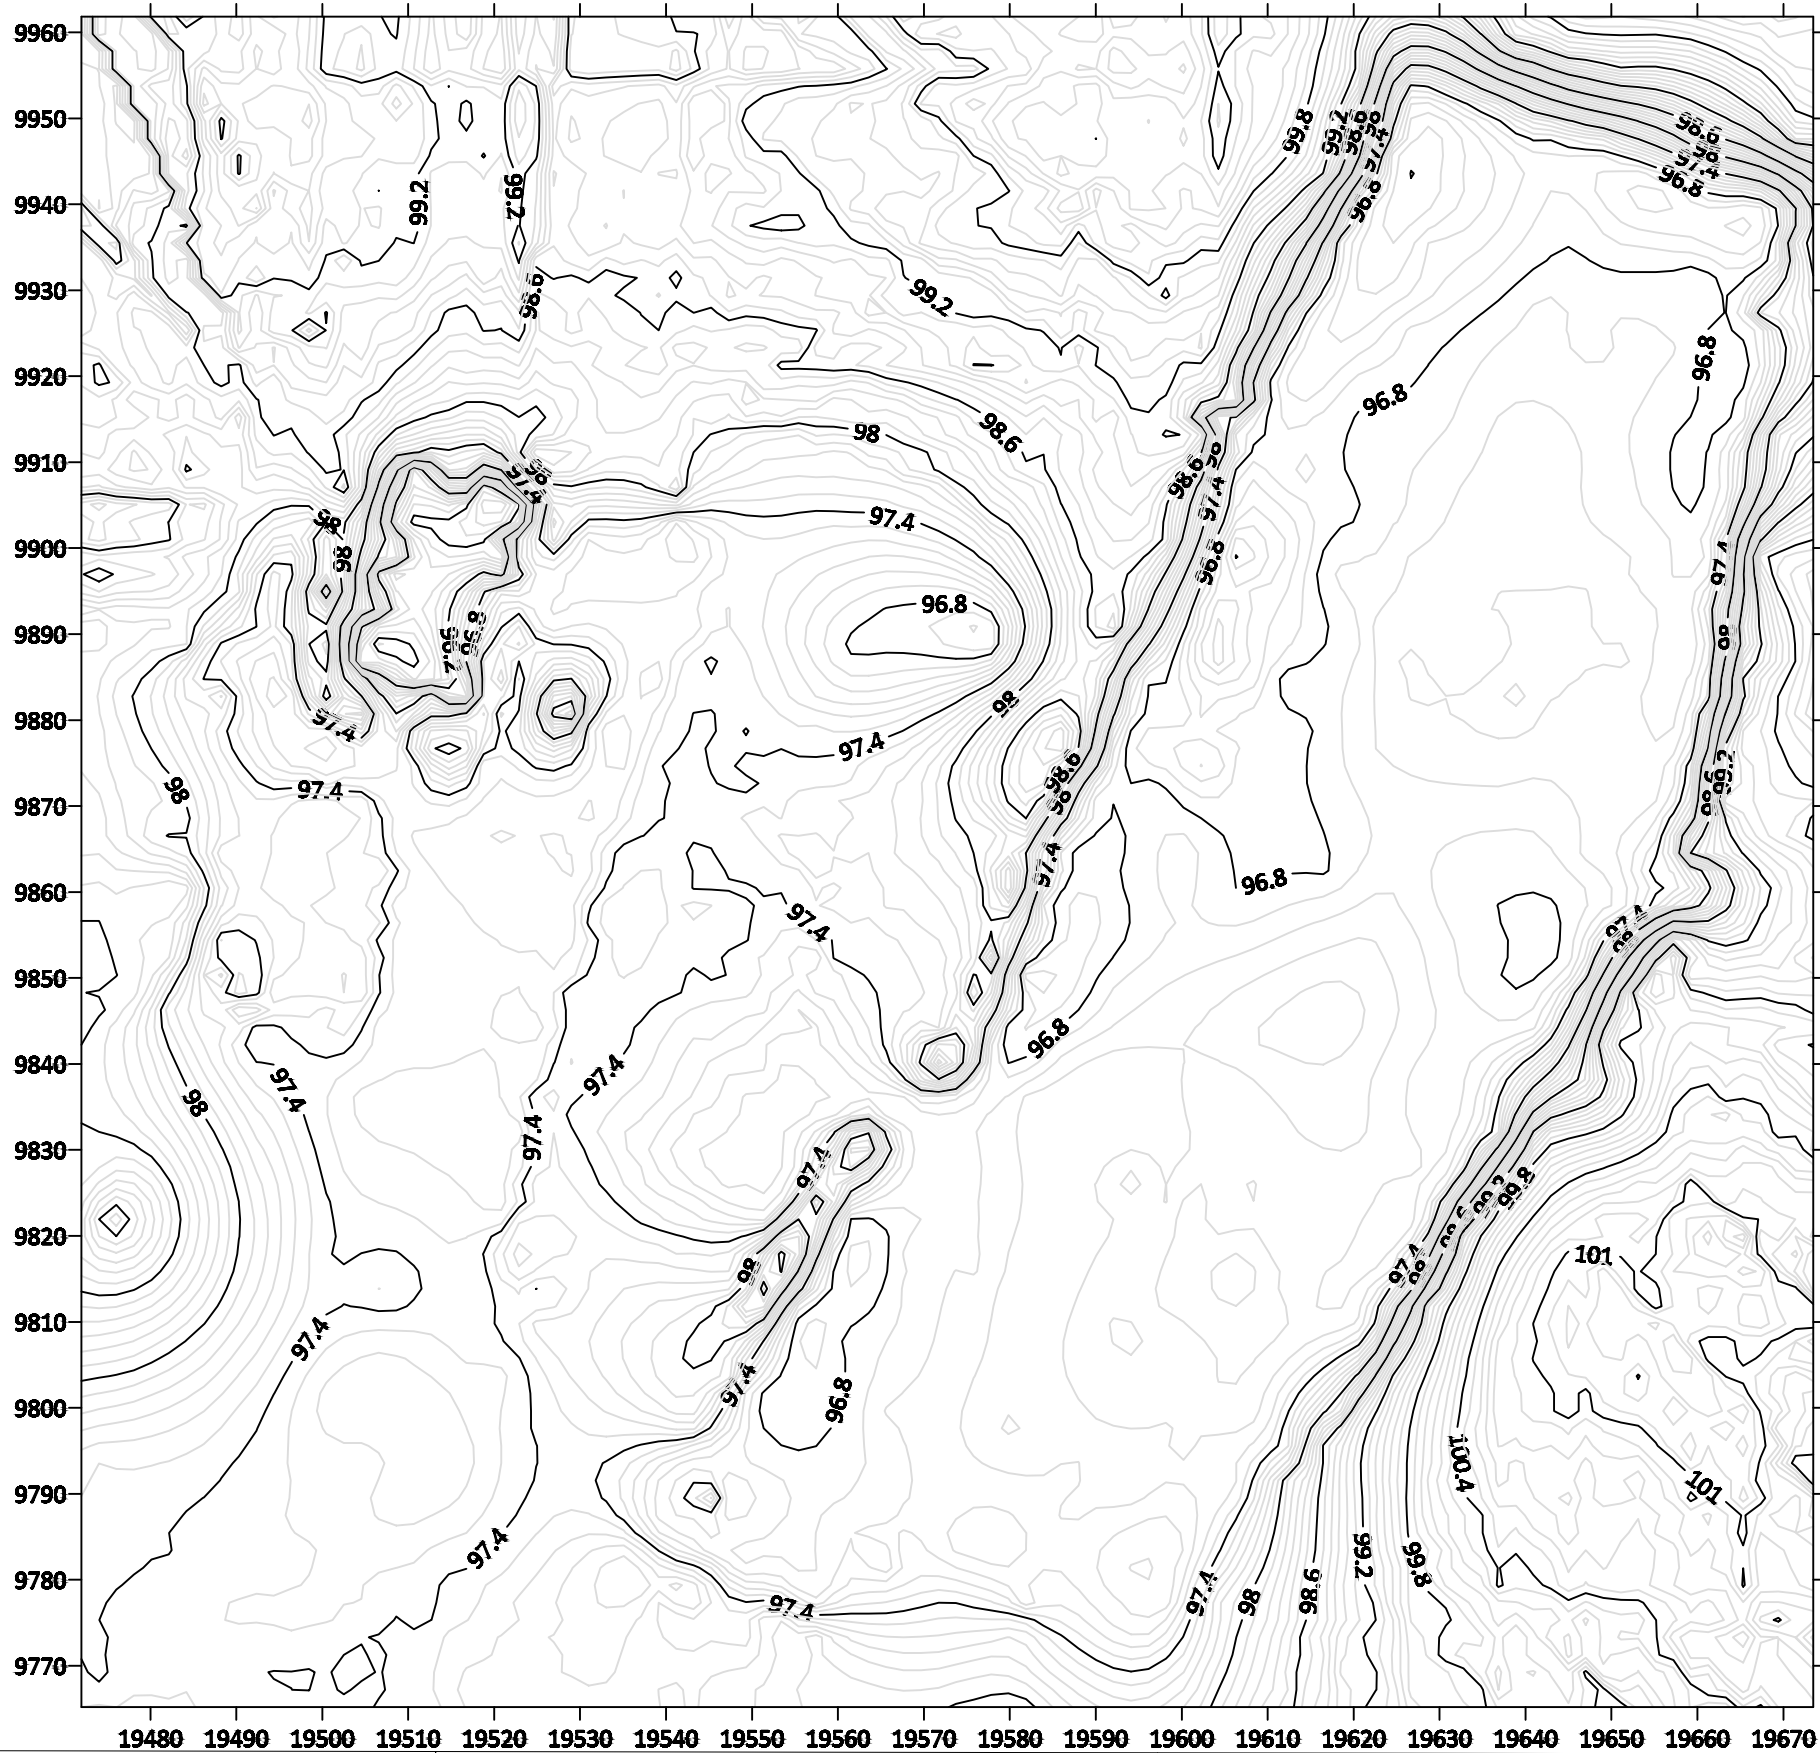

NAME / GROUP NAME : Mr. Sukith Siriwardana/ GROUP 01

GROUP MEMBERS : D/ENG/23/0078/CE NMYP Premaratne
D/ENG/24/0020/CE B.Banujan
D/ENG/24/0112/CE M.F.Hasni Ahamed
D/ENG/24/0038/CE GDTD Jayawardena
D/ENG/24/0077/CE MKCK Madawala
D/ENG/24/0104/CE KKVYA Vidanage

DRAWING DETAILS				DRAWING TITLE	
DATE	2025/10/30	UNITS	METERS	CONTOUR	
LOCATION	COMBAT TRAINING AREA,SLNS VIDURA, EASTERN NAVAL COMMAND BASE, SAMPOOR TRINCOMALEE.	DRAWING NO.	02		
NOTES	This drawing and related data are part of an academic survey and design study conducted for educational purposes at SLNS Vidura. The information contained herein is not to be copied, distributed, or used for any purpose other than project evaluation without prior written permission from the supervising authorities and the Department of Civil Engineering,ADU.			PROJECT	
				SURVEY CAMP INTAKE 41	

DEPARTMENT OF CIVIL
ENGINEERING
FACULTY OF ENGINEERING
GENERAL SIR JOHN KOTELAWALA
DEFENCE UNIVERSITY